




1 EXISTING ROOF FRAMING PLAN

- EXISTING FRAMING SHOWN IS APPROXIMATE. VERIFY IN FIELD ALL EXISTING BEAM SIZES, TYPES, SPANS, SPACING, ETC. PRIOR TO CONSTRUCTION.
- COORDINATE ALL ROOFTOP UNITS WITH MECHANICAL DRAWINGS.


2 NEW BEAM BEARING AT EXISTING CMU

SCALE: 3/4\" = 1'-0"

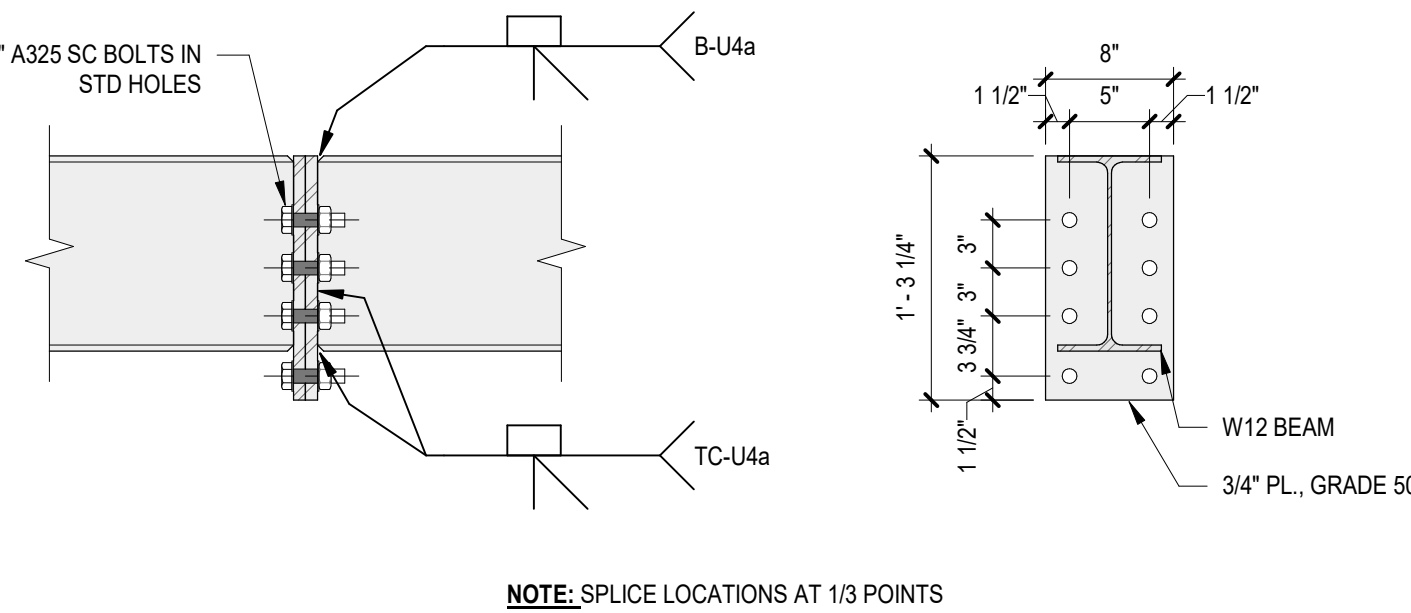


4 BEAM SPLICE

SCALE: 1\" = 1'-0"

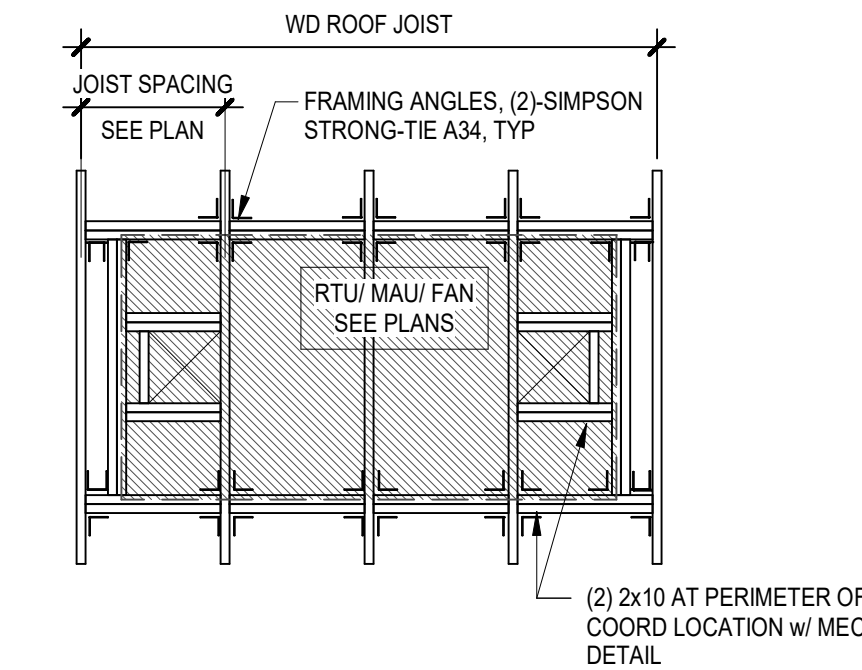

6 TYPICAL MECHANICAL UNIT SUPPORT

SCALE: 3/8\" = 1'-0"

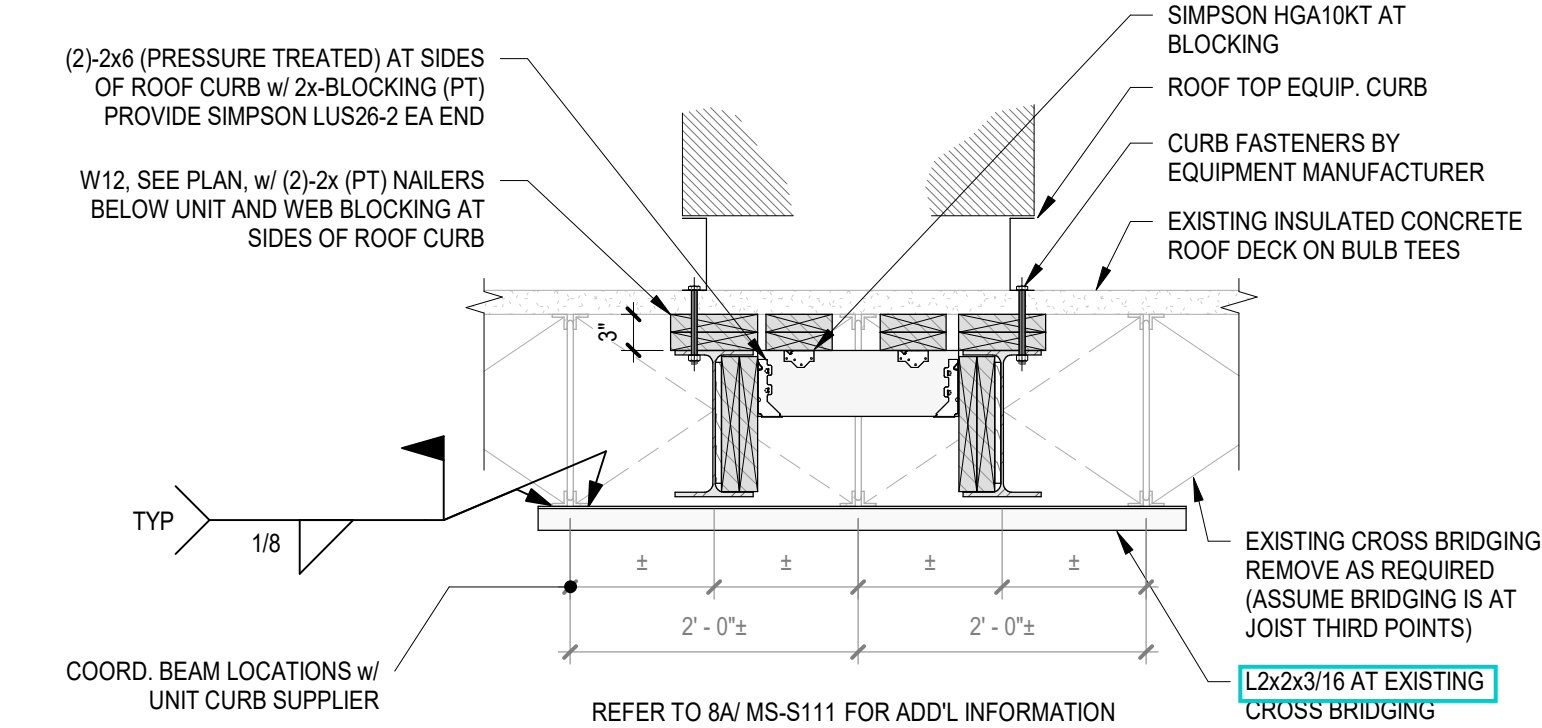

8 SECTION AT FRAMING

SCALE: 3/4\" = 1'-0"

MASONRY OPENING (M.O.)	MASONRY WALL THICKNESS		
	4"	6"	12"
3'-0"	L3-1/2x3-1/2x1/4	(2)L3-1/2x2-1/2x1/4	(2)L3-1/2x3-1/2x1/4
4'-0"	L4x3-1/2x1/4	(2)L4x2-1/2x1/4	(2)L4x3-1/2x1/4
6'-0"	L5x3-1/2x5/16	(2)L5x2-1/2x5/16	(2)L5x3-1/2x5/16
8'-0"	L6x3-1/2x5/16	(2)L6x2-1/2x5/16	(2)L6x3-1/2x5/16


- NOTES:**
- INTELS IN EXTERIOR WALLS SHALL BE HOT-DIPPED GALVANIZED.
 - ANGLES SHALL BE LONG-LEG VERTICAL UNLESS NOTED OTHERWISE.
 - BEARING LENGTH AT EACH END SHALL BE 8" MINIMUM.
 - INTELS IN EXTERIOR WALLS SHALL HAVE A MINIMUM THICKNESS OF 5/16".
 - COORDINATE EXACT SIZE, LOCATION AND QUANTITY WITH ARCHITECTURAL, MECHANICAL AND ELECTRICAL DWG's.

9 TYPICAL NON-BEARING-WALL LOOSE LINTEL SCHEDULE

SCALE: 3/4\" = 1'-0"


3 NEW BEAM BEARING AT EXISTING CLAY TILE

SCALE: 3/4\" = 1'-0"

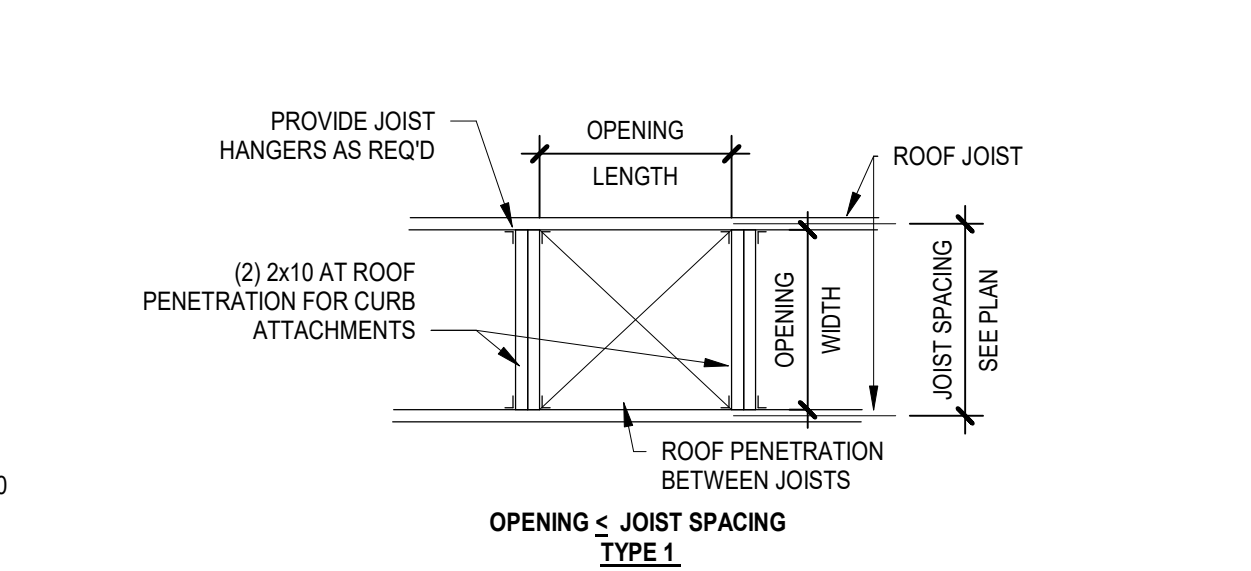


5 TYPICAL WOOD ROOF PENETRATION

SCALE: 1/2\" = 1'-0"

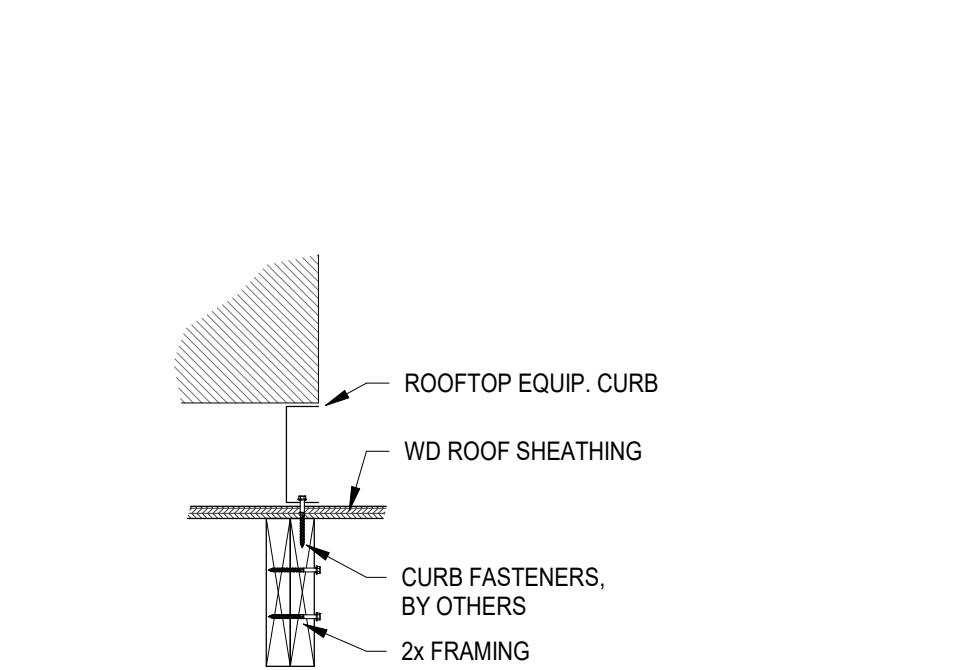


7 DETAIL AT CURB

SCALE: 1\" = 1'-0"

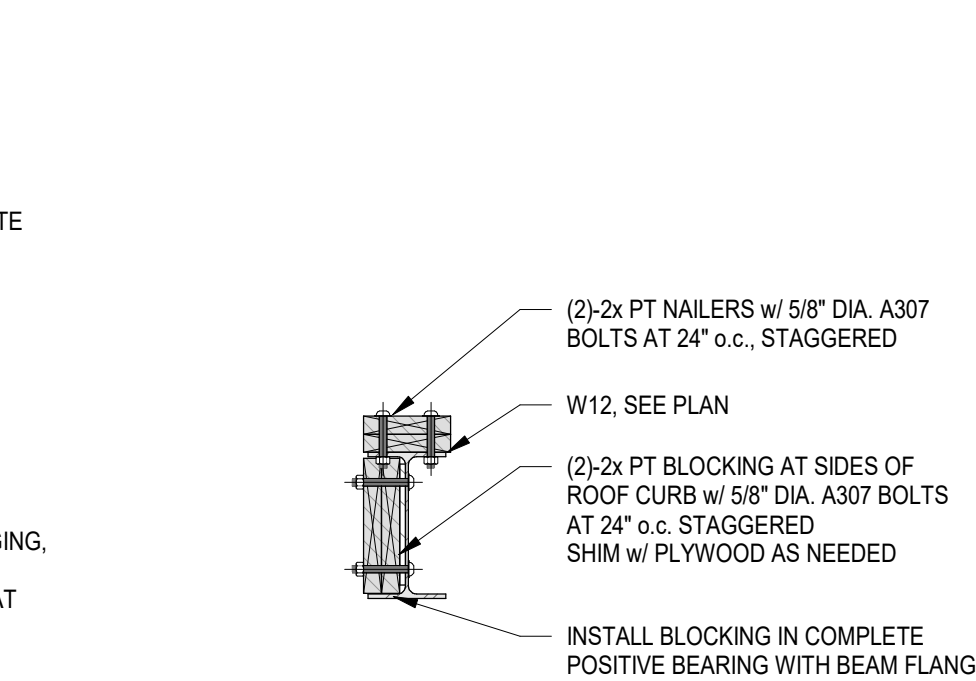

8A BLOCKING AND NAILER FASTENING

SCALE: 3/4\" = 1'-0"

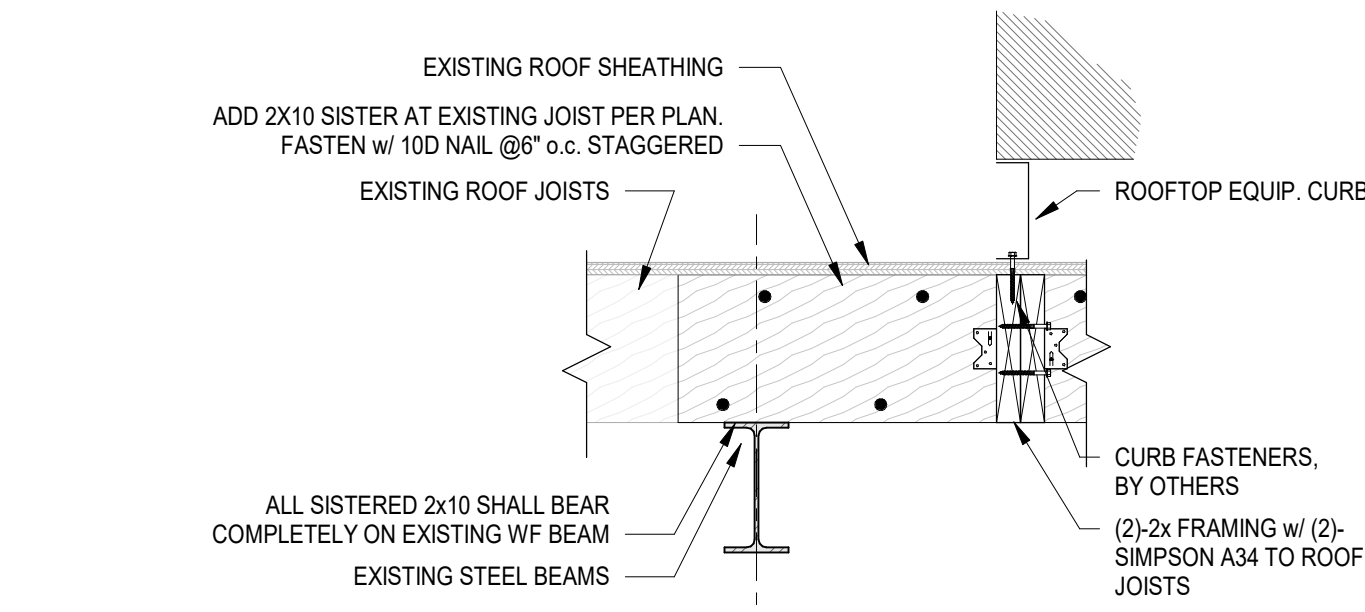

10 TYPICAL WOOD JOIST REINFORCEMENT

SCALE: 1\" = 1'-0"



LYNDONVILLE CENTRAL
SCHOOLS
ELEMENTARY SCHOOL
MAIN STREET LYNDONVILLE, NY
14098

SED #: 45-10-01-04-0-001-018
SED #: 45-10-01-04-0-002-009

2023 CAPITAL IMPROVEMENT
PROJECT PHASE 2
CONSTRUCTION DOCUMENTS



237 Main Street, Suite 500
Buffalo, NY 14202
www.wendelcompanies.com
p.716.688.0766 tf.877.293.6335

Wendel WD Architecture, Engineering, Surveying and
Landscape Architecture, P.C.

NOTE:
THIS DOCUMENT AND THE EXISTING CONDITIONS INCORPORATED HEREIN, AS AN INSTRUMENT OF PROFESSIONAL SERVICE, IS THE PROPERTY OF THE ARCHITECT AND ENGINEER AND IS NOT TO BE USED IN WHOLE OR IN PART FOR ANY OTHER PROJECT WITHOUT THE WRITTEN AUTHORIZATION OF THE ARCHITECT AND ENGINEER. UNAUTHORIZED ALTERATION OR ADDITION TO ANY SURVEY, DRAWING, DESIGN, SPECIFICATION, PLAN OR REPORT IS PROHIBITED IN ACCORDANCE WITH STATE LAW, CODE AND RULES.


NO.	REVISIONS	DATE
1	ISSUED FOR BIDS	11-12-2023
2		
3		
4		
5		
6		
7		
8		
9		
10		

DWS:FILE

ROOF FRAMING PLAN AND
DETAILS

DATE	SCALE	DWN.	DWS	CHK.	MAW/JDM
11-12-2023	As indicated				
PROJ. No. 628101					
DWG. No.					

MS-S111

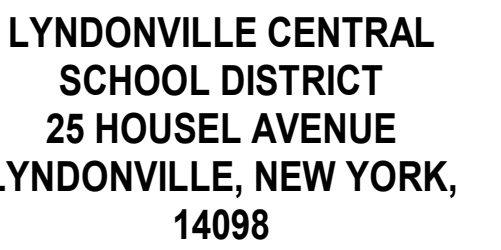

**23 CAPITAL IMPROVEMENT
PROJECT PHASE 2
CONSTRUCTION DOCUMENTS**

