

**2023 CAPITAL IMPROVEMENT  
PROJECT PHASE 2  
CONSTRUCTION DOCUMENTS**



- ## 2 NEW BEAM BEARING AT EXISTING CMU

SCALE: 3/4" = 1'-0"



SCALE: 3/4" = 1'-0"



SCALE: 1" = 1'-0"



SCALE: 1/2" = 1'-0"



SCALE: 1" = 1'-0"



SCALE: 3/8" = 1'-0"



SCALE: 1" = 1'-0"



SCALE: 3/4" = 1'-0"

## 8A BLOCKING AND NAILER FASTENING

8A




SCALE: 3/4" = 1'-0"



10

|     |                |            |
|-----|----------------|------------|
|     |                |            |
|     |                |            |
| 0   | ISSUED FOR BID | 11-12-2025 |
| NO. | REVISIONS      | DATE       |

## ROOF FRAMING PLAN AND DETAILS

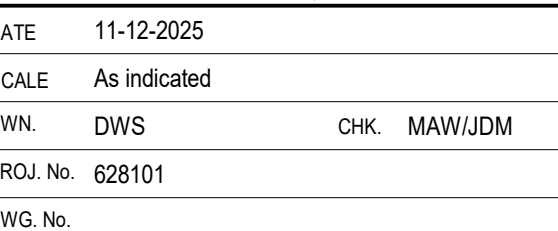





## 1 GYMNASIUM REINFORCEMENT ROOF FRAMING PLAN

SCALE: 1/8" = 1'-0"

### PARTIAL ROOF FRAMING PLAN NOTES



- EXISTING FRAMING SIZES AND LOCATIONS SHOWN ARE APPROXIMATE. VERIFY EXISTING CONDITIONS IN THE FIELD AND NOTIFY ENGINEER OF DISCREPANCIES.
- CONTRACTOR TO VERIFY IN FIELD EXISTING ANGLE FRAME CONDITIONS AT ROOF TOP UNITS TO BE REPLACED. NOTIFY ENGINEER OF EXISTING CONDITIONS. DEMOLISH EXISTING ANGLE FRAMES IF REQUIRED AND REPLACE WITH NEW ANGLE FRAMES. STEEL FRAMES ARE REQUIRED AT UNSUPPORTED UNIT AND PENETRATION EDGES.
- REFER TO MECHANICAL DRAWINGS FOR INFORMATION RELATED TO ROOFTOP-MOUNTED EQUIPMENT AND PENETRATIONS.
- EQUIPMENT WEIGHTS SHOWN INCLUDE AN ALLOWANCE FOR UNIT CURB WEIGHT. SUBMIT CURB AND UNIT DATA, INCLUDING WEIGHTS, TO ENGINEER FOR REVIEW.
- INDICATES AREA OF EXISTING ROOF OPENINGS TO BE INFILLED WITH 1 1/2"x18ga GALV (G60) TYPE B METAL ROOF DECK.

| KEYNOTE LEGEND |   |
|----------------|---|
| NO.            | COMMENTS   |
| 1              | COMMERCIALLY BLAST CLEAN EXISTING EXPOSED STEEL FRAMING. REMOVE ALL RUST DOWN TO BARE METAL PER SSPC-SP10/NAACE 2 NEAR-WHITE SPECIFICATIONS. PRIME AND PAINT EXISTING STEEL FRAMING w/ A HIGH-PERFORMANCE COATING SYSTEM PER SPECIFICATION DIVISION 09.01 REQUIREMENTS. |
| 2              | EXISTING UNIT TO BE REPLACED. COORD. w/ MECH. AND RE-USE EXISTING ANGLE CHANNEL FRAME FOR UNIT CURB SUPPORT.   |




## 7 44LH JOIST ELEVATION

SCALE: 1/4" = 1'-0"

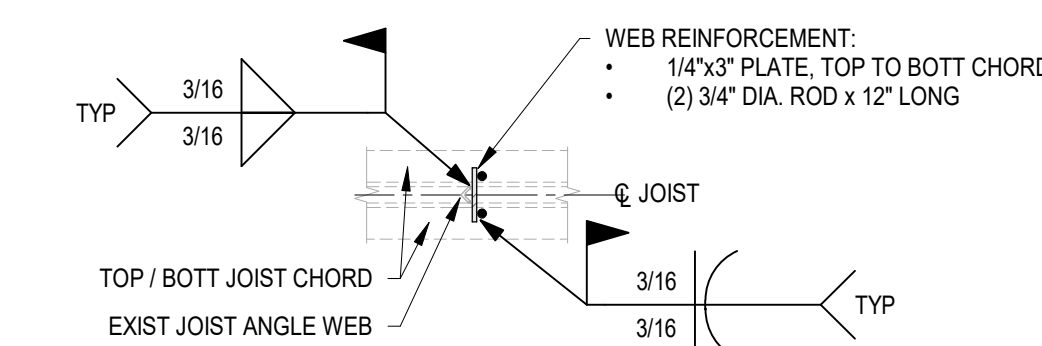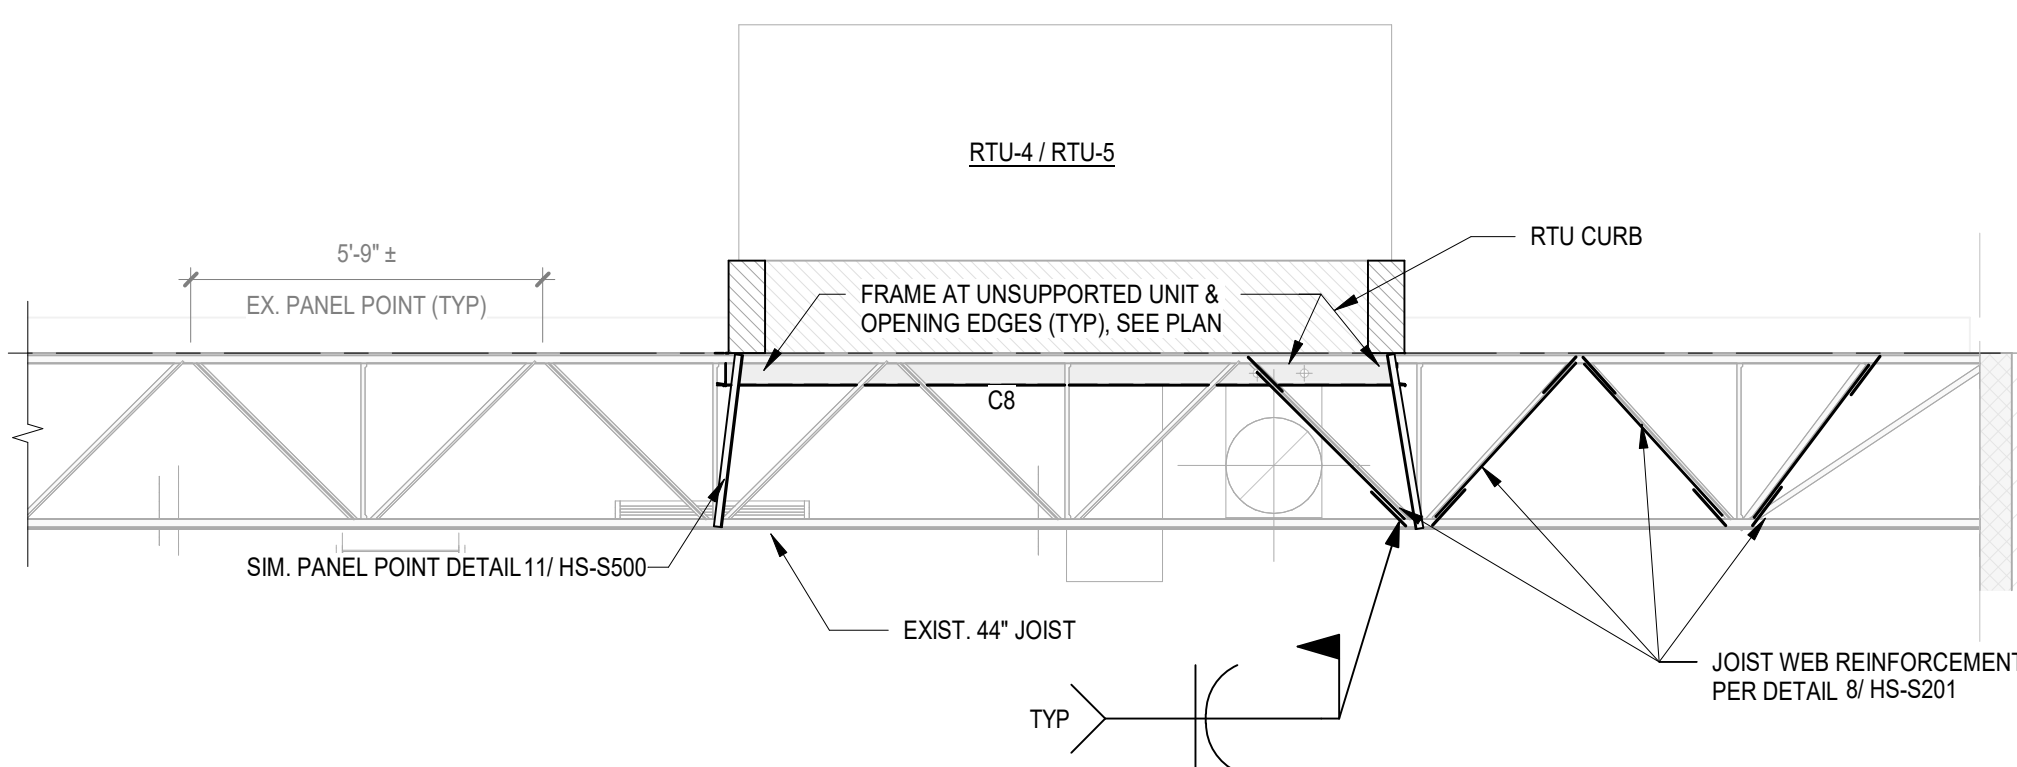


## 8 EXISTING JOIST REINFORCEMENT WITH ANGLE WEB DETAIL

SCALE: 3/4" = 1'-0"

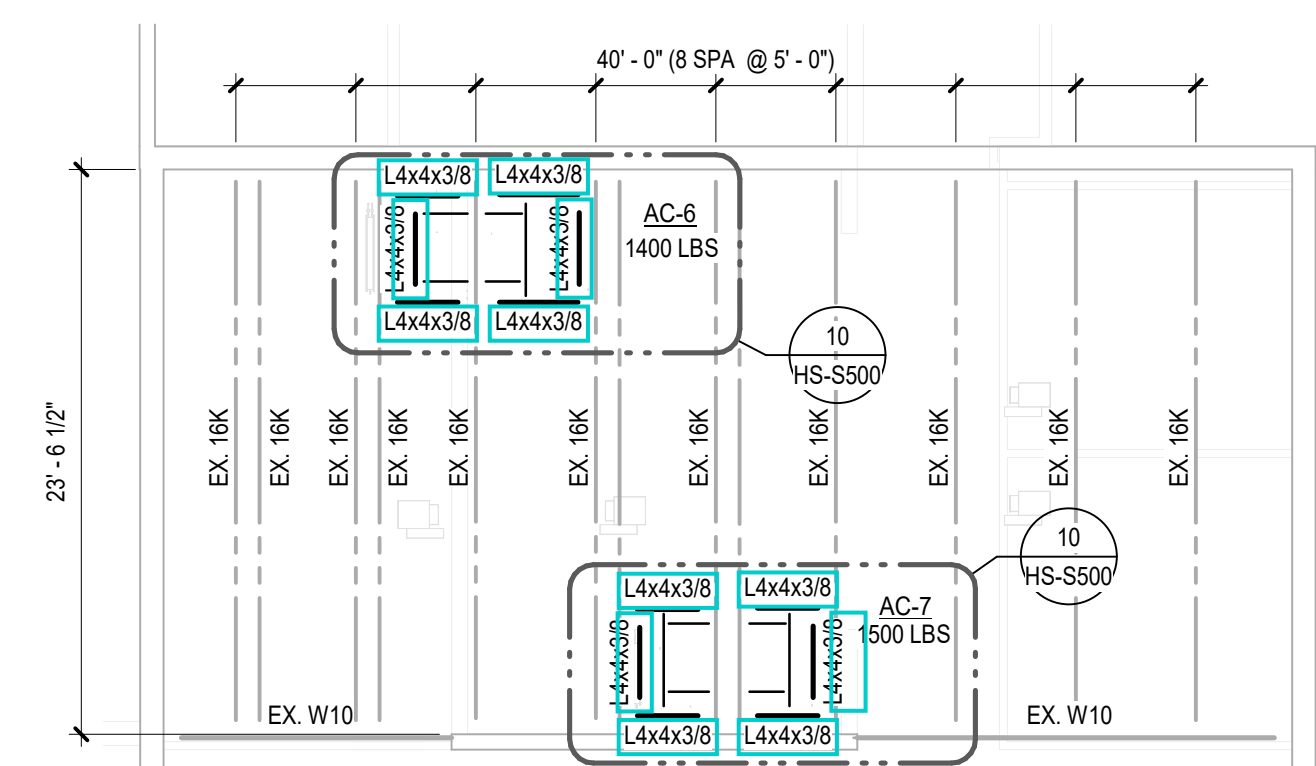


## 5 RTU SUPPORT FRAMING AC-6 & AC-7

SCALE: 1/8" = 1'-0"

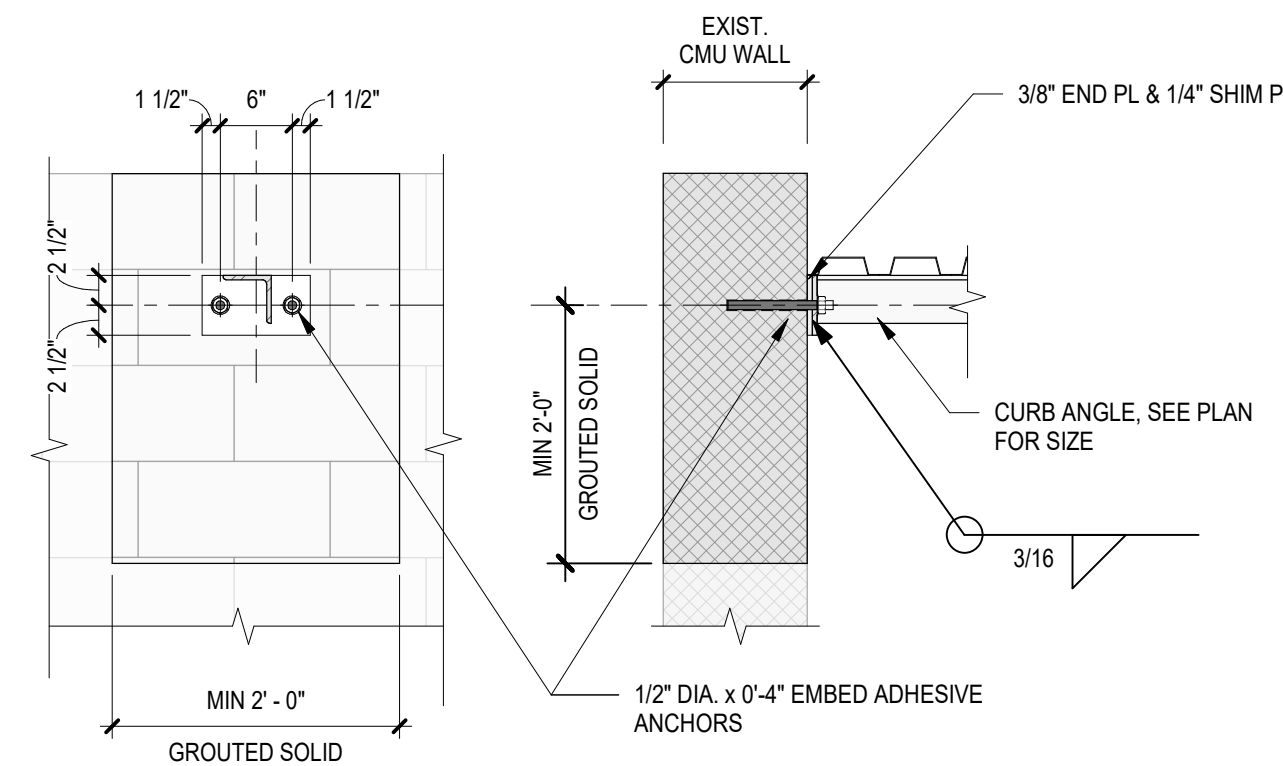


## 6 TYPICAL PLATE CONNECTION TO EXISTING WALL

SCALE: 3/4" = 1'-0"

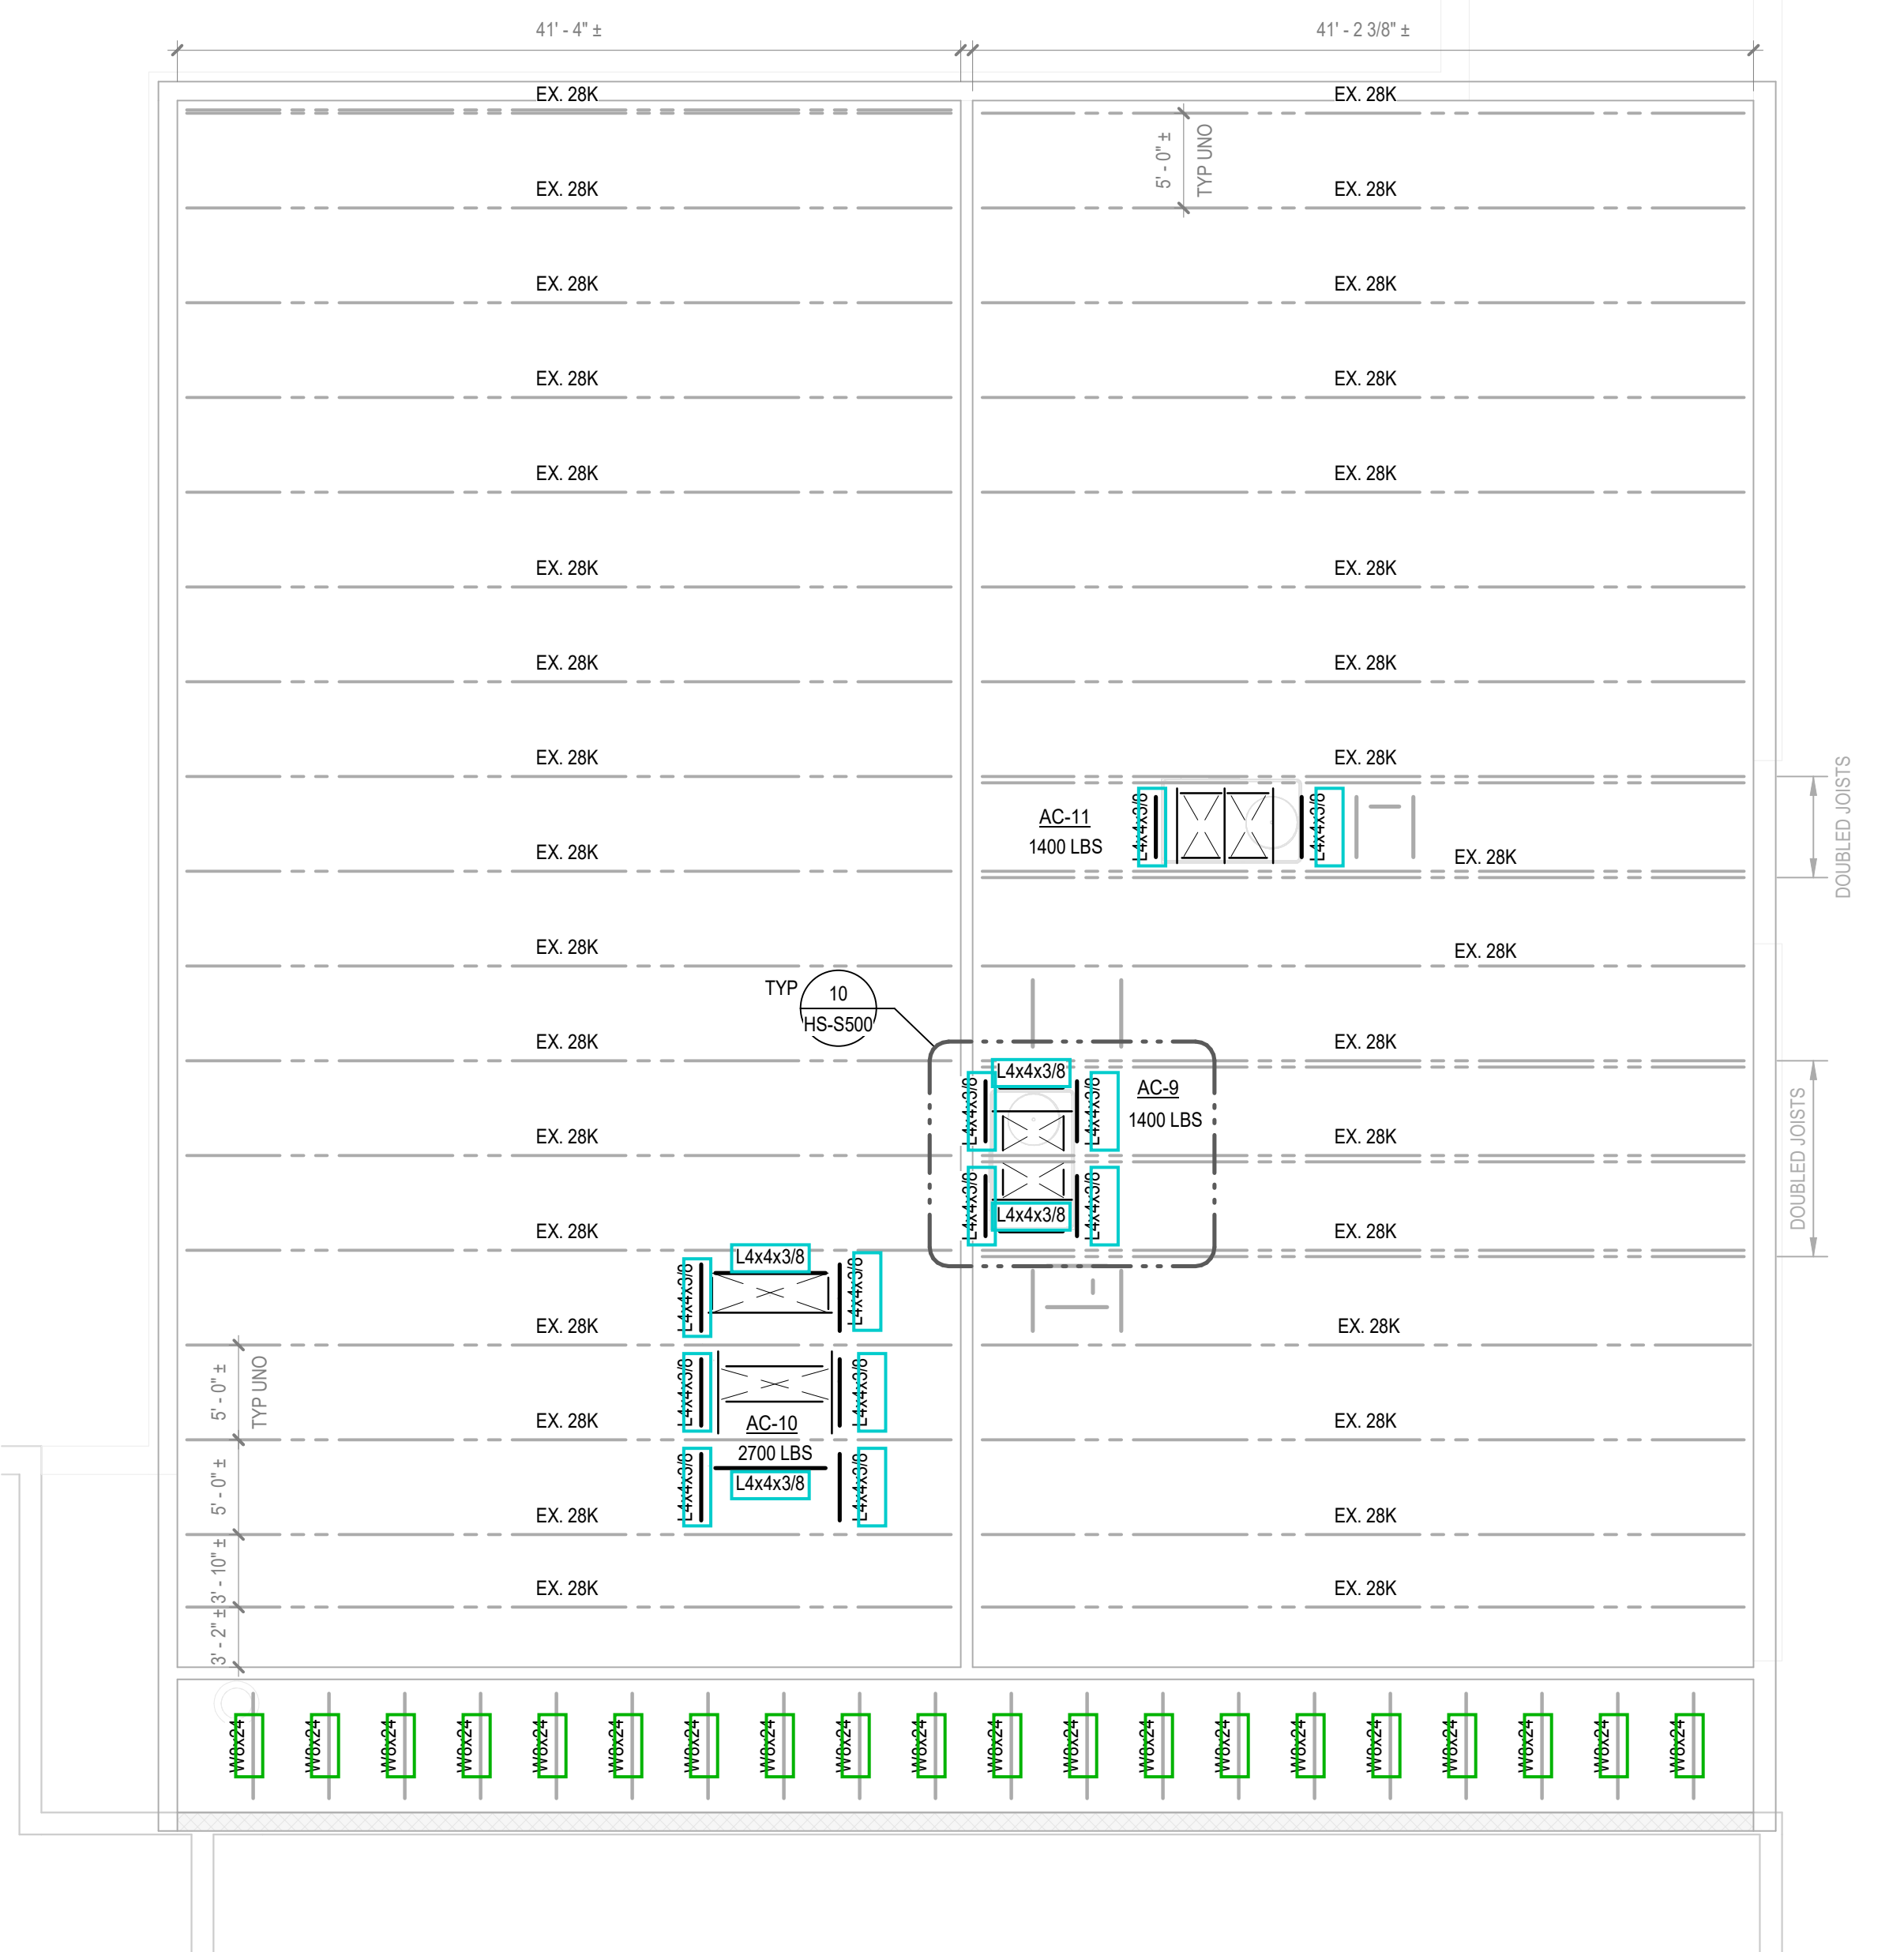


## 2 RTU SUPPORT MUSIC WING

SCALE: 1/8" = 1'-0"

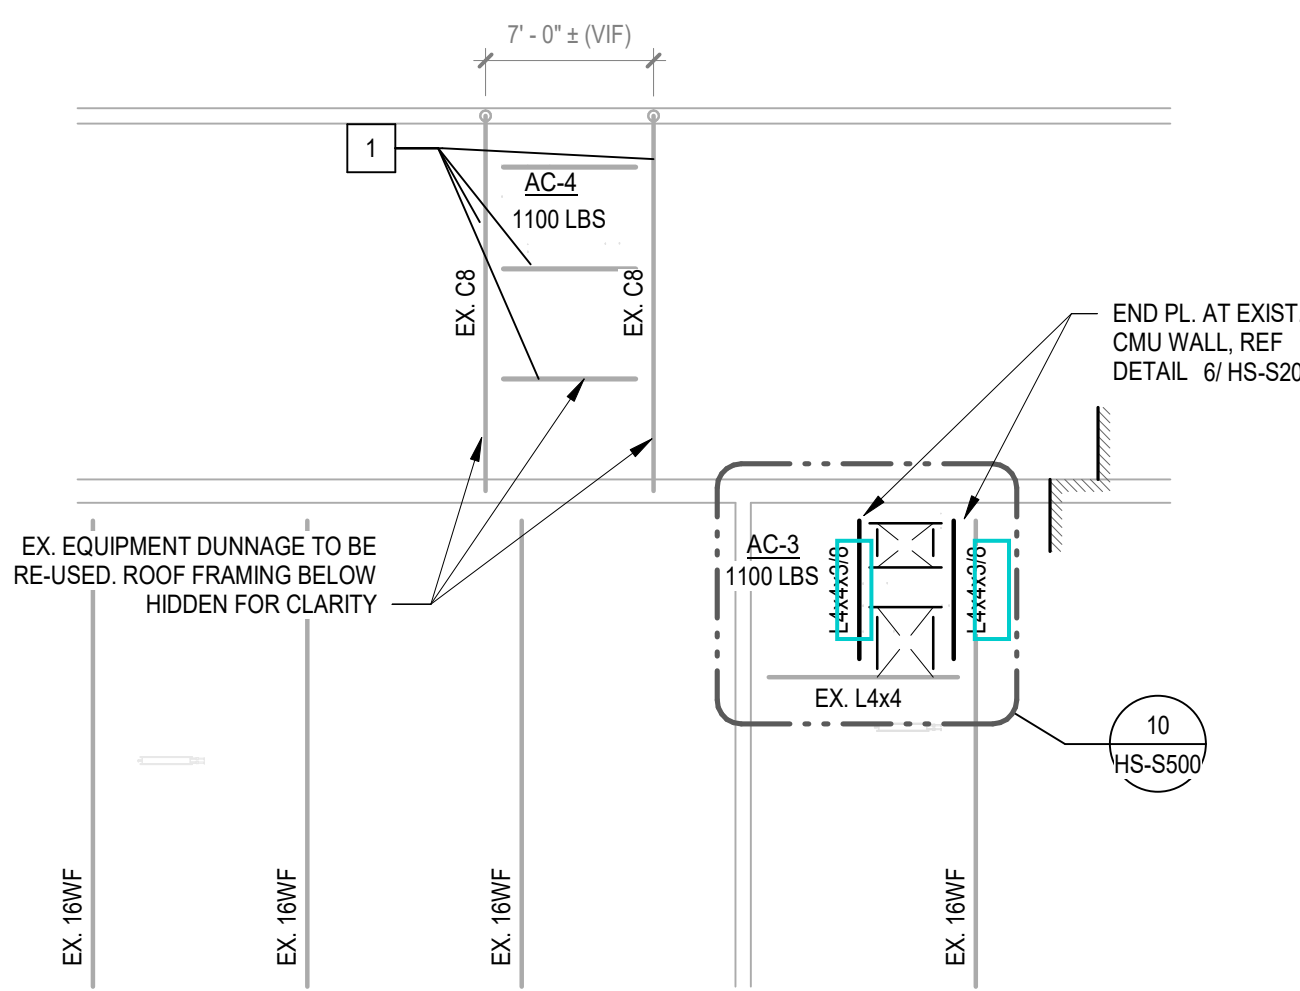

## 3 RTU SUPPORT FRAMING AC-4 & AC-5

SCALE: 1/8" = 1'-0"

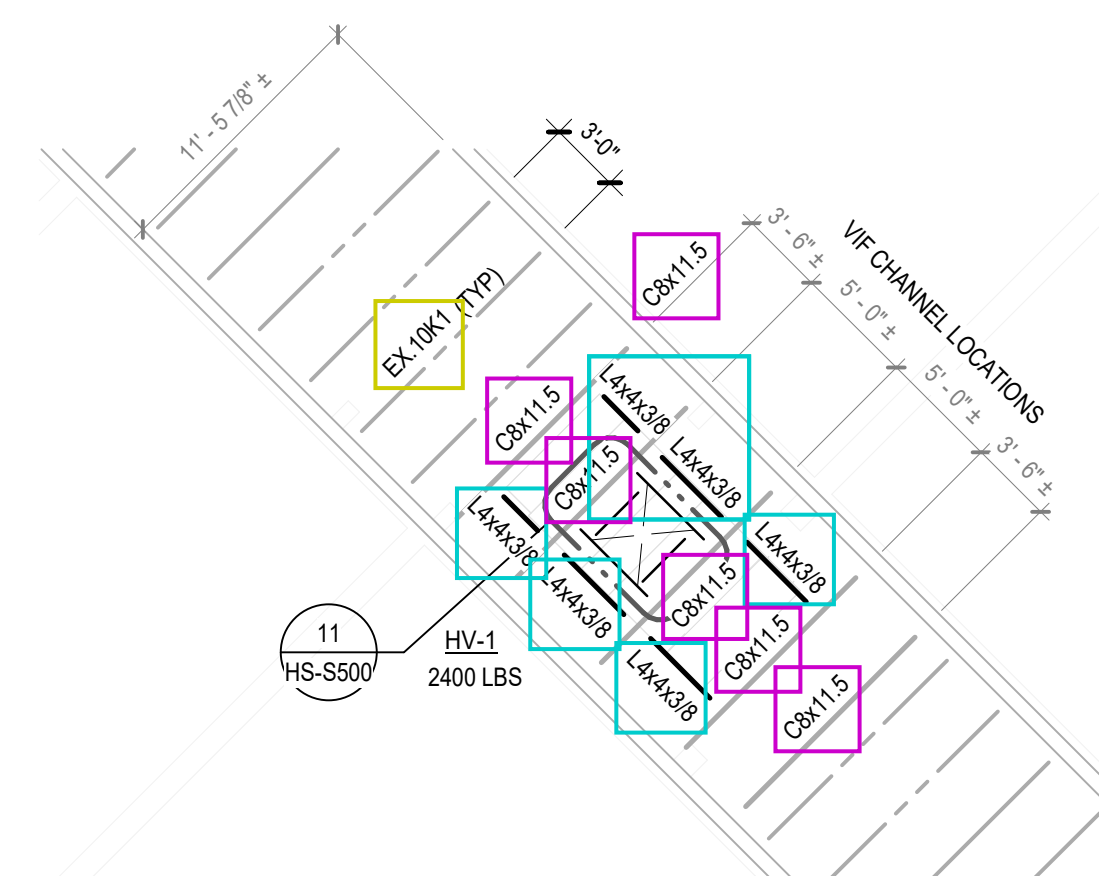

## 4 RTU AC-16 SUPPORT FRAMING

SCALE: 1/8" = 1'-0"



LYNDONVILLE CENTRAL  
SCHOOL DISTRICT  
25 HOUSEL AVENUE  
LYNDONVILLE, NEW YORK,  
14098


SED #: 45-10-01-04-0-001-018  
SED #: 45-10-01-04-0-002-009

2023 CAPITAL IMPROVEMENT  
PROJECT PHASE 2  
CONSTRUCTION DOCUMENTS



Centerpointe Corporate Park  
375 Essjay Road, Suite 200  
Williamsville, NY 14221  
www.wendelcompanies.com  
p.716.688.0766 tf.877.293.6335

Wendel W.D. Architecture, Engineering, Surveying and  
Landscape Architecture, P.C.

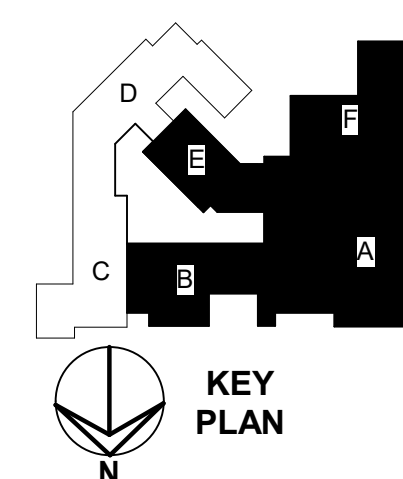


KEY  
PLAN

NOTE:  
THIS DOCUMENT, AND THE EXISTING CONDITIONS INCORPORATED HEREIN, AS AN INSTRUMENT OF PROFESSIONAL SERVICE, IS THE PROPERTY OF THE ARCHITECT AND ENGINEER AND IS NOT TO BE USED IN WHOLE OR IN PART FOR ANY OTHER PROJECT WITHOUT THE WRITTEN AUTHORIZATION OF THE ARCHITECT AND ENGINEER. UNAUTHORIZED ALTERATION OR ADDITION TO ANY SURVEY, DRAWING, DESIGN, SPECIFICATION, PLAN OR REPORT IS PROHIBITED IN ACCORDANCE WITH STATE LAW, CODE AND RULES.

| NO. | ISSUED FOR R/S | DATE |
|-----|----------------|------|
| 1   | 11-12-2023     |      |

DWS: TLE

PARTIAL ROOF FRAMING PLANS

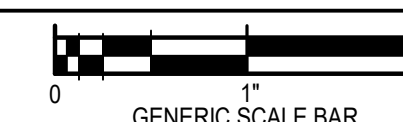

SCALE BAR SHOWN IS TWO INCHES ON THE ORIGINAL DRAWING  
IF NOT TWO INCHES ON THIS SHEET, ADJUST ACCORDINGLY

|           |              |
|-----------|--------------|
| DATE      | 11-12-2023   |
| SCALE     | As indicated |
| DWN       | DWS          |
| PROJ. No. | 628101       |
| DWG. No.  |              |

CHK: MAW / JDM

HS-S201