


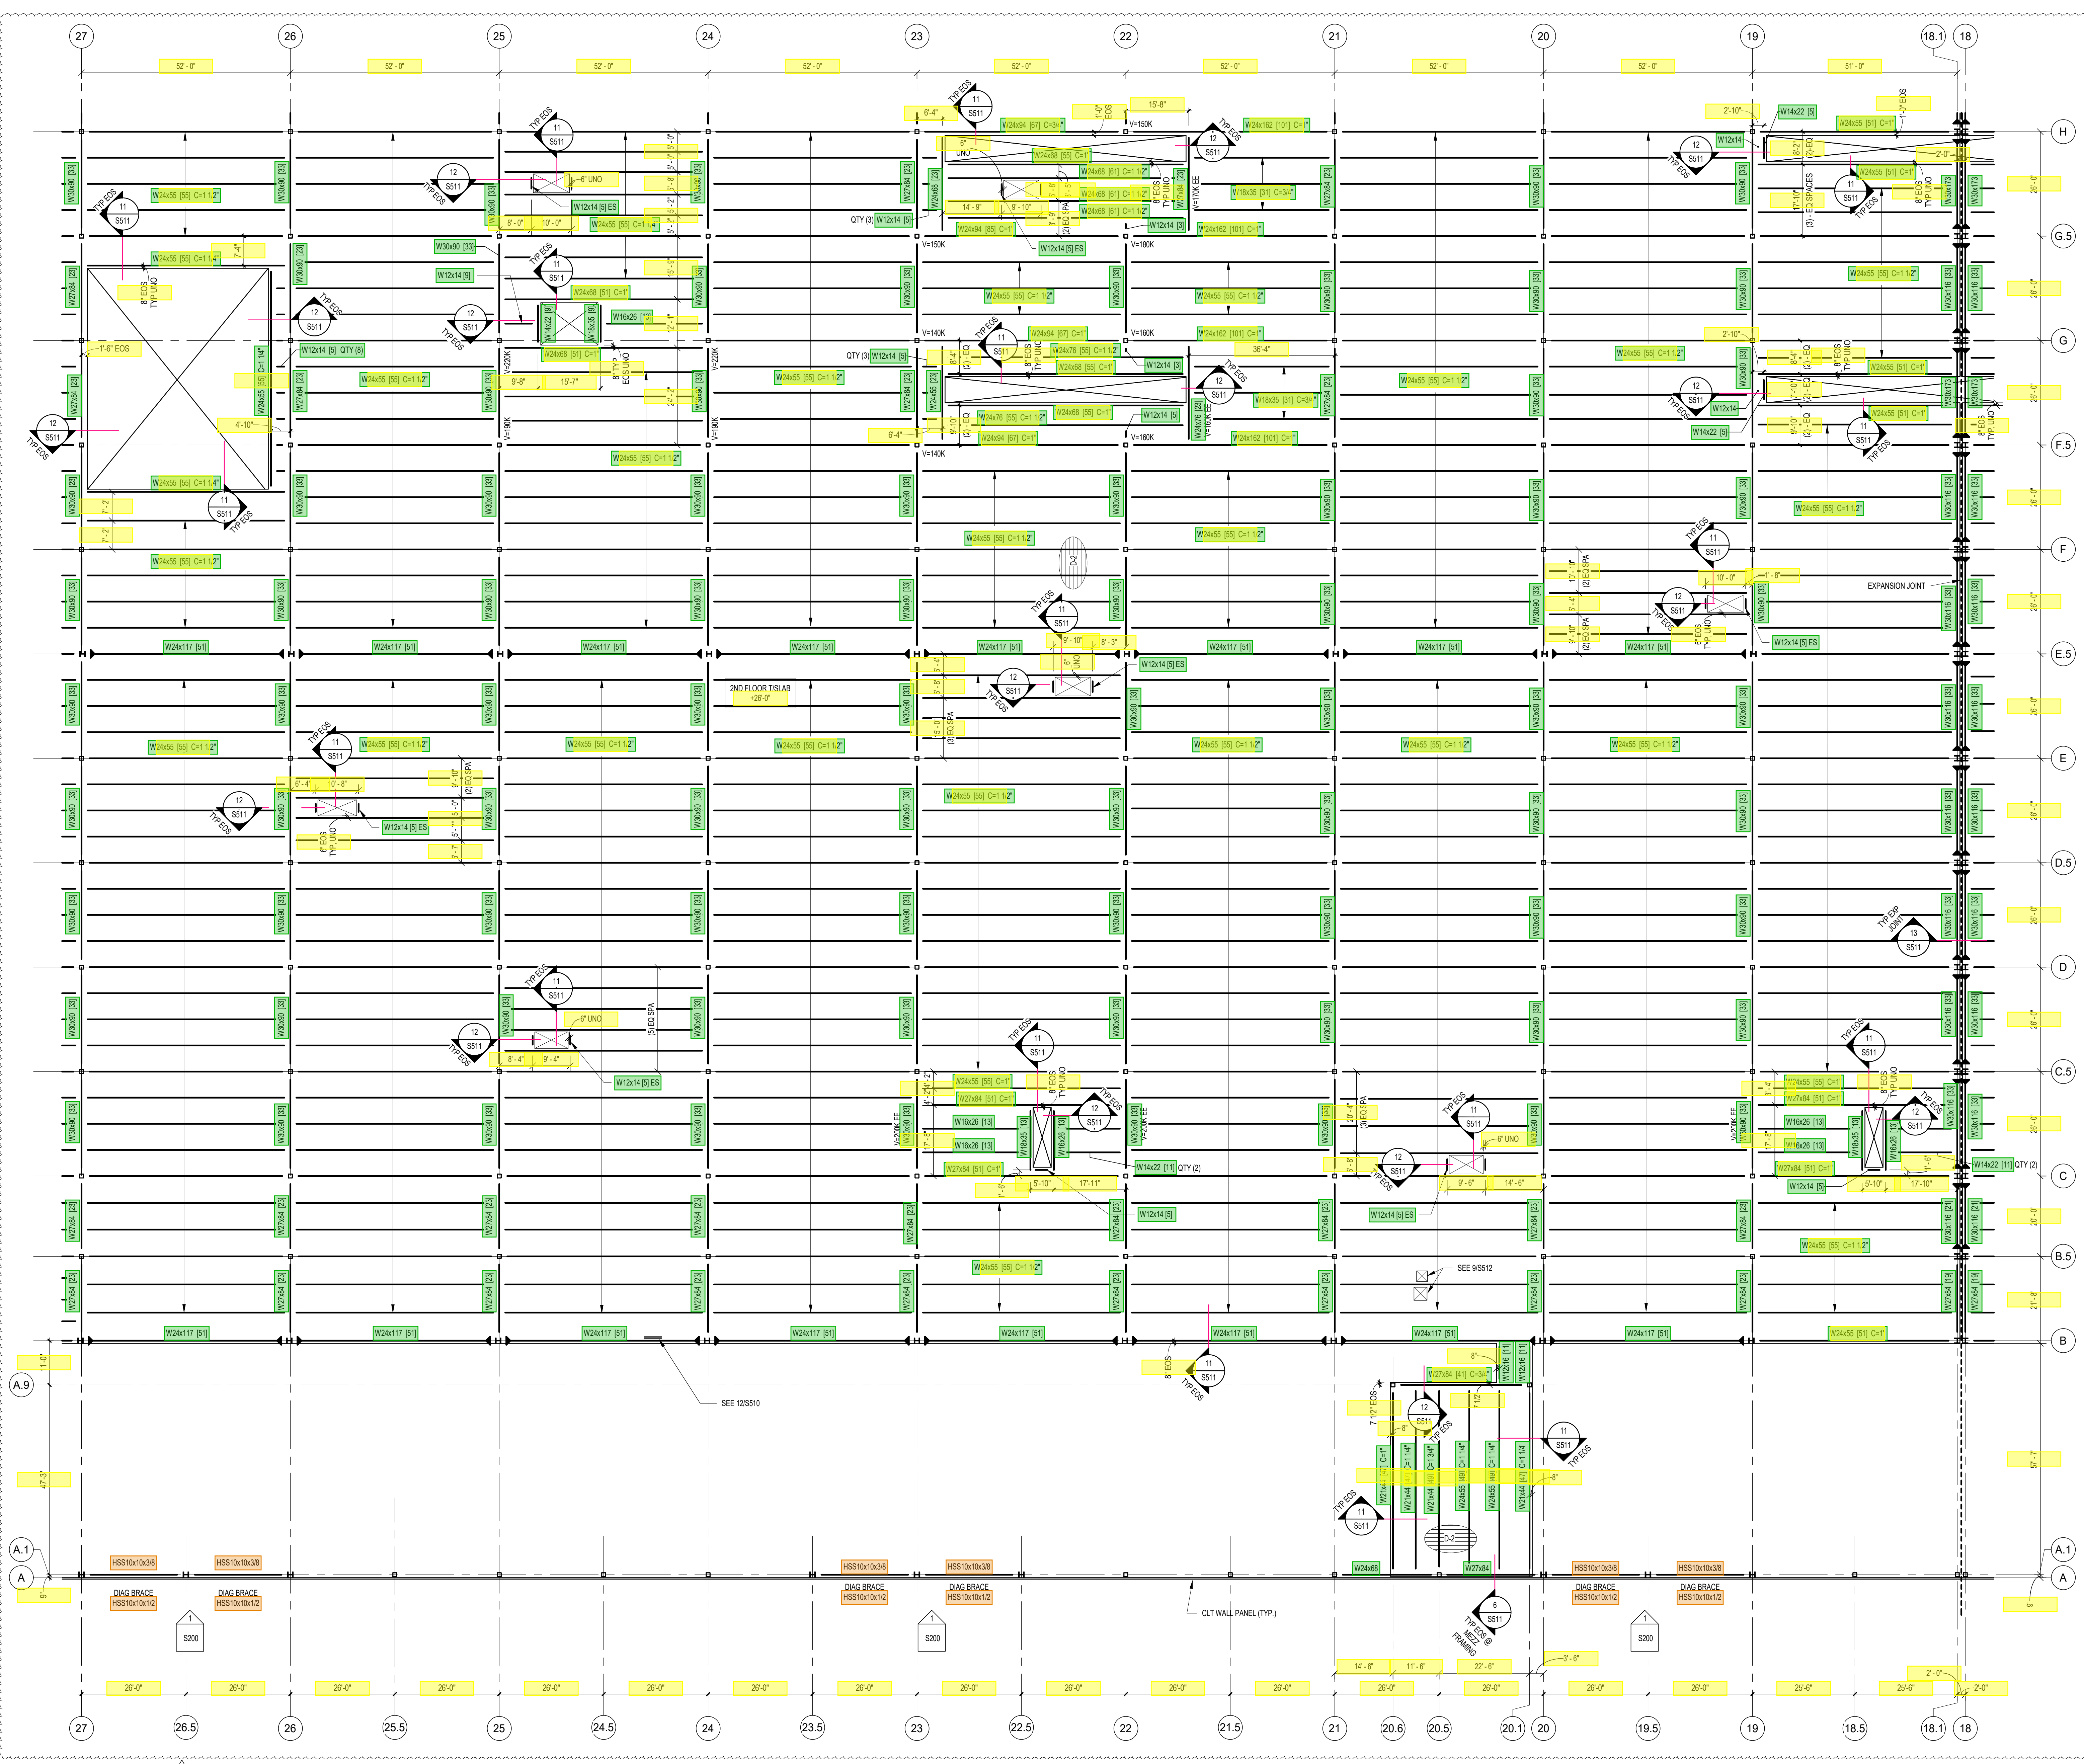

PARTIAL SPINE 2ND FLOOR FRAMING PLAN - AREA B1
S101.2B1
Scale: 1/16" = 1'-0"

2ND FLOOR FRAMING PLAN NOTES:

- TOP OF STEEL ELEVATION FOR 2ND FLOOR CONSTRUCTION IS (+25'-6") ABOVE DATUM FIRST FLOOR ELEVATION, UNLESS NOTED OTHERWISE BY +/- FROM 2ND FLOOR ELEVATION.
- SEE DECK SCHEDULE ON S600 FOR FLOOR CONSTRUCTION DETAILS.
- THE STEEL FABRICATOR SHALL DESIGN END SHEAR CONNECTIONS TO RESIST LRFD END REACTIONS DENOTED AS V=XXX ON BEAM LABELS. SEE TABLES ON SHEET S512 FOR REACTIONS NOT SHOWN.
- FOR SIZES AND LOCATIONS OF FLOOR PENETRATIONS, SEE ARCHITECTURAL, MECHANICAL, AND PLUMBING DRAWINGS. MAJOR PENETRATIONS ARE DETAILED ON PLAN. FOR MINOR PENETRATIONS COOR LOCATIONS AND SIZE W/ ARCH/MEP/ME AND SEE S511 FOR APPLICABLE FRAMING DETAILS.
- (XX) DENOTES NUMBER OF 3/4" DIA. SHEAR STUDS FOR COMPOSITE SLAB TO BEAM CONNECTION. SEE DECK SCHEDULE FOR LENGTH.
- ALL STAIR FRAMING SHALL BE DESIGNED BY THE STAIR MANUFACTURER.
- ◀ DENOTES FULLY RESTRAINED MOMENT CONNECTION. SEE 1/SS12 FOR DETAILS.
- SEE STRUCTURAL ELEVATIONS ON S200 FOR VERTICAL BRACING, GIRTS, HEADERS AND ADDITIONAL FRAMING INFORMATION.
- PROVIDE (2) #3 BAR X 5'-0" AT REINTRA SLAB CORNERS. SEE DETAIL S510.
- COORDINATE ALL DIMENSIONS WITH ARCHITECTURAL DRAWINGS.
- SEE S512 FOR MHE JUMPER BEAM DETAIL REQUIRED BELOW MHE POST LOADS ON MEZZ > 5 KIPS.

PROJECT

HUMMINGBIRD
CENTRAL HUB GEN1.0 V1.1
2134 BLUE CREEK ROAD
HOGANSVILLE, GA 30230

CLIENT

SEEFRED DEV. MANAGEMENT INC.
3333 RIVERWOOD PKWY, SUITE 200
ATLANTA, GA 30339

ARCHITECT

ARCHITECT OF RECORD
AECOM
800 Gessner Rd
Houston, TX 77024
281.646.2400 tel
www.aecom.com

ENGINEERS/CONSULTANTS

STRUCTURAL
AECOM
277 Nationwide Blvd
Columbus, OH 43215
281.646.2400 tel
www.aecom.com

MEP
AECOM
800 Gessner Rd
Houston, TX 77024
281.646.2400 tel
www.aecom.com

IT / SECURITY
AECOM
800 Gessner Rd
Houston, TX 77024
281.646.2400 tel
www.aecom.com


FIRE PROTECTION / ALARM
AECOM
800 Gessner Rd
Houston, TX 77024
281.646.2400 tel
www.aecom.com

REGISTRATION



03/07/2025

KEYPLAN

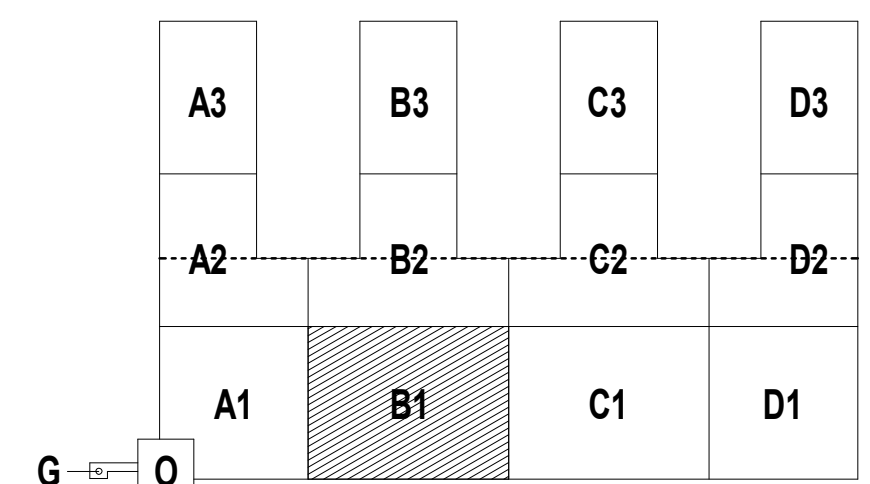

REV	DATE	ISSUED BY	TO	DESCRIPTION
1	11/15/2024	AECOM	AHJ	ISSUE FOR BID & PERMIT
4	03/07/2025	AECOM	ATHEVA	ADDENDUM #3

PROJECT NUMBER

60735057

SHEET TITLE

PARTIAL SPINE
STRUCTURAL SECOND
FLOOR FRAMING PLAN -
AREA B1

SHEET NUMBER

S101.2B1

